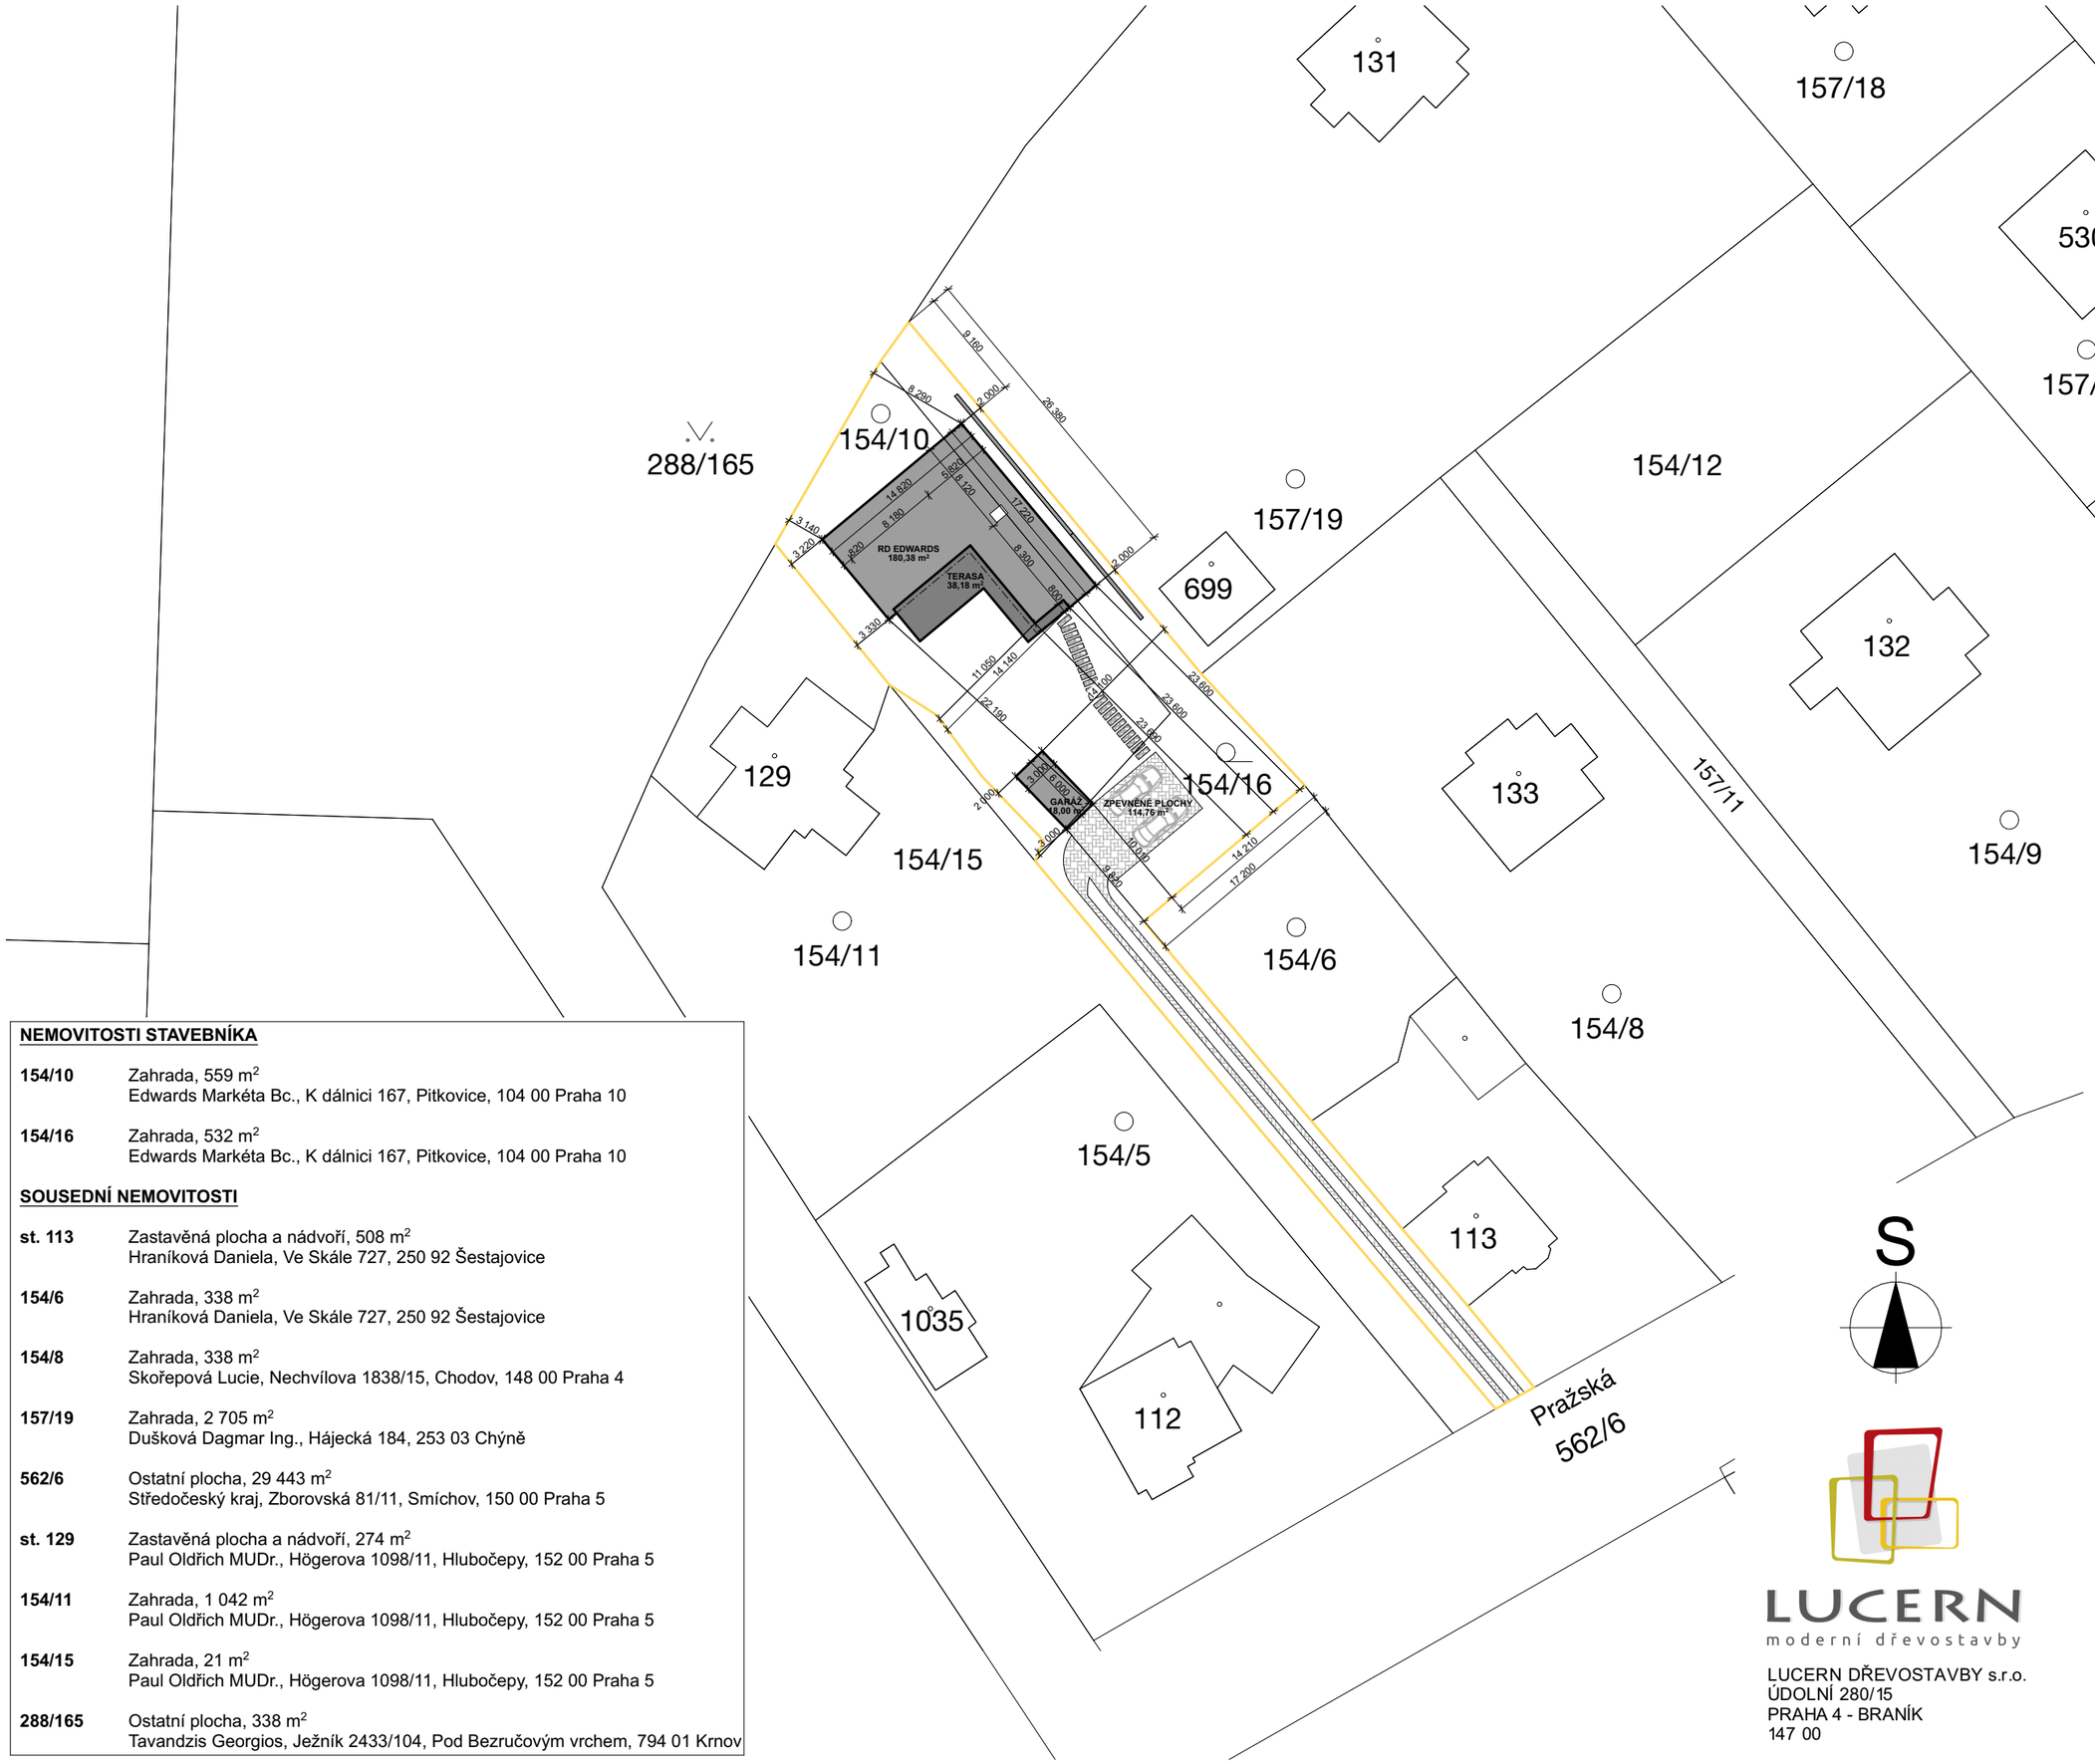

NEMOVITOSTI STAVEBNÍKA

154/10	Zahrada, 559 m² Edwards Markéta Bc., K dálnici 167, Pitkovice, 104 00 Praha 10
154/16	Zahrada, 532 m² Edwards Markéta Bc., K dálnici 167, Pitkovice, 104 00 Praha 10

SOUSEDNÍ NEMOVITOSTI

st. 113	Zastavěná plocha a nádvoří, 508 m² Hraníková Daniela, Ve Skále 727, 250 92 Šestajovice
154/6	Zahrada, 338 m² Hraníková Daniela, Ve Skále 727, 250 92 Šestajovice
154/8	Zahrada, 338 m² Skořepová Lucie, Nechvílova 1838/15, Chodov, 148 00 Praha 4
157/19	Zahrada, 2 705 m² Dušková Dagmar Ing., Hájecká 184, 253 03 Chýně
562/6	Ostatní plocha, 29 443 m² Středočeský kraj, Zborovská 81/11, Smíchov, 150 00 Praha 5
st. 129	Zastavěná plocha a nádvoří, 274 m² Paul Oldřich MUDr., Högerova 1098/11, Hlubočepy, 152 00 Praha 5
154/11	Zahrada, 1 042 m² Paul Oldřich MUDr., Högerova 1098/11, Hlubočepy, 152 00 Praha 5
154/15	Zahrada, 21 m² Paul Oldřich MUDr., Högerova 1098/11, Hlubočepy, 152 00 Praha 5
288/165	Ostatní plocha, 338 m² Tavandzis Georgios, Ježník 2433/104, Pod Bezručovým vrchem, 794 01 Krnov

LUCERN
moderní dřevostavby

LUCERN DŘEVOSTAVBY s.r.o.
ÚDOLNÍ 280/15
PRAHA 4 - BRANÍK
147 00

± 0,000 = 397,402 m. n. m. (Bpv)

INVESTOR
Bc. Markéta Edwards,
K dálnici 167, Pitkovice,
104 00 Praha 10

STAVBA
NOVOSTAVBA RODINNÉHO DOMU
č. parc.: 154/10 a 154/16
k.ú.: Jevany [659312]

OBEC
Jevany [533378]

STUPEŇ PD
DSP + DPS

VEDOUCÍ PROJEKTU
Ing. Josef Frydrýn

VYPRACOVAL
Ing. Václav Křepelák, DiS.

AUTORIZACE
Ing. Miloš Slavík

DATUM
09/2025

MĚŘÍTKO
1:500

VÝKRES
SITUACE CELKOVÁ

C.2.

Digitálně podepsal Ing. Miloš Slavík
Datum: 2026.03.09 08:46:08 +01'00'