ELEKTRO
NAPOJENÍ ELETŘINY BUDE PROVEDENO DO ELETROMĚROVÉ SKŘÍNĚ NA HRANICI POZEMKU.
ELEKTROMĚR JE OSAZEN U POZEMKU STAVEBNÍKA.
KANALIZACE
SPLAŠKOVÉ VODY BUDOU GRAVITAČNĚ SVÁDĚNY DO KANALIZAČNÍ ŠACHTY A NÁSLEDNĚ DO KANALIZAČNÍHO ŘADU.
VODA
NAPOJENÍ Z VODOVODNÍHO ŘADU PŘES VODOMĚRNOU ŠACHTU.

POZNÁMKY:

PLOCHA POZEMKU CELKEM:	1 091,00 m²
ZASTAVĚNÁ PLOCHA RD:	180,38 m²
ZPEVNĚNÉ PLOCHY, TERASA, GARÁŽ:	170,94 m²
ZASTAVĚNOST POZEMKU:	15,67 %
ZBYLÁ ZELENÁ PLOCHA POZEMKU:	84,33 %

LEGENDA:
- HRANICE POZEMKU DLE KN
- STÁVAJÍCÍ VEDENÍ NÍZKÉHO NAPĚTÍ DO 1 kV
- STÁVAJÍCÍ PŘÍPOJKA DO ELEKTRO PILÍŘE 0,84 m
- NAVRŽENÁ DOMOVNÍ PŘÍPOJKA ELEKTRA 82,15 m
- STÁVAJÍCÍ PŘÍPOJKA SPLAŠKOVÉ KANALIZACE 8,15 m
- NAVRŽENÁ DOMOVNÍ PŘÍPOJKA SPLAŠKOVÉ KANALIZACE 39,91 m
- STÁVAJÍCÍ VEDENÍ VODOVODU
- STÁVAJÍCÍ PŘÍPOJKA VODOVODU 4,96 m
- NAVRŽENÁ DOMOVNÍ PŘÍPOJKA VODOVODU 80,97 m
- NAVRŽENÁ DOMOVNÍ PŘÍPOJKA DEŠŤOVÉ KANALIZACE 57,40 m
- OPLOCENÍ - HRANICE POZEMKU DLE KN - STÁVAJÍCÍ, DRÁTĚNÉ, S BETONOVÝMI SLOUPKY
- OPLOCENÍ ULIČNÍ - STÁVAJÍCÍ, DRÁTĚNÉ, S BETONOVÝMI SLOUPY
- POŽÁRNĚ NEBEZPEČNÝ PROSTOR OD FASÁDY OBJEKTU

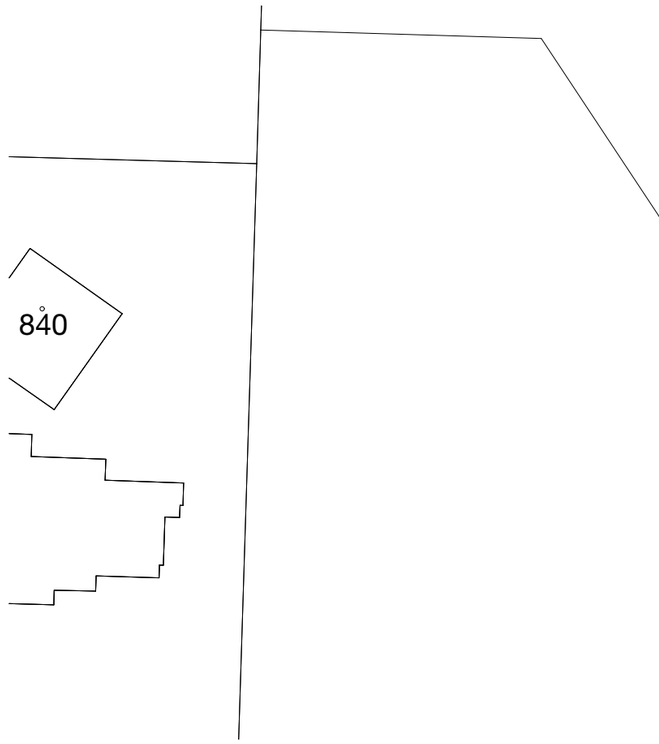

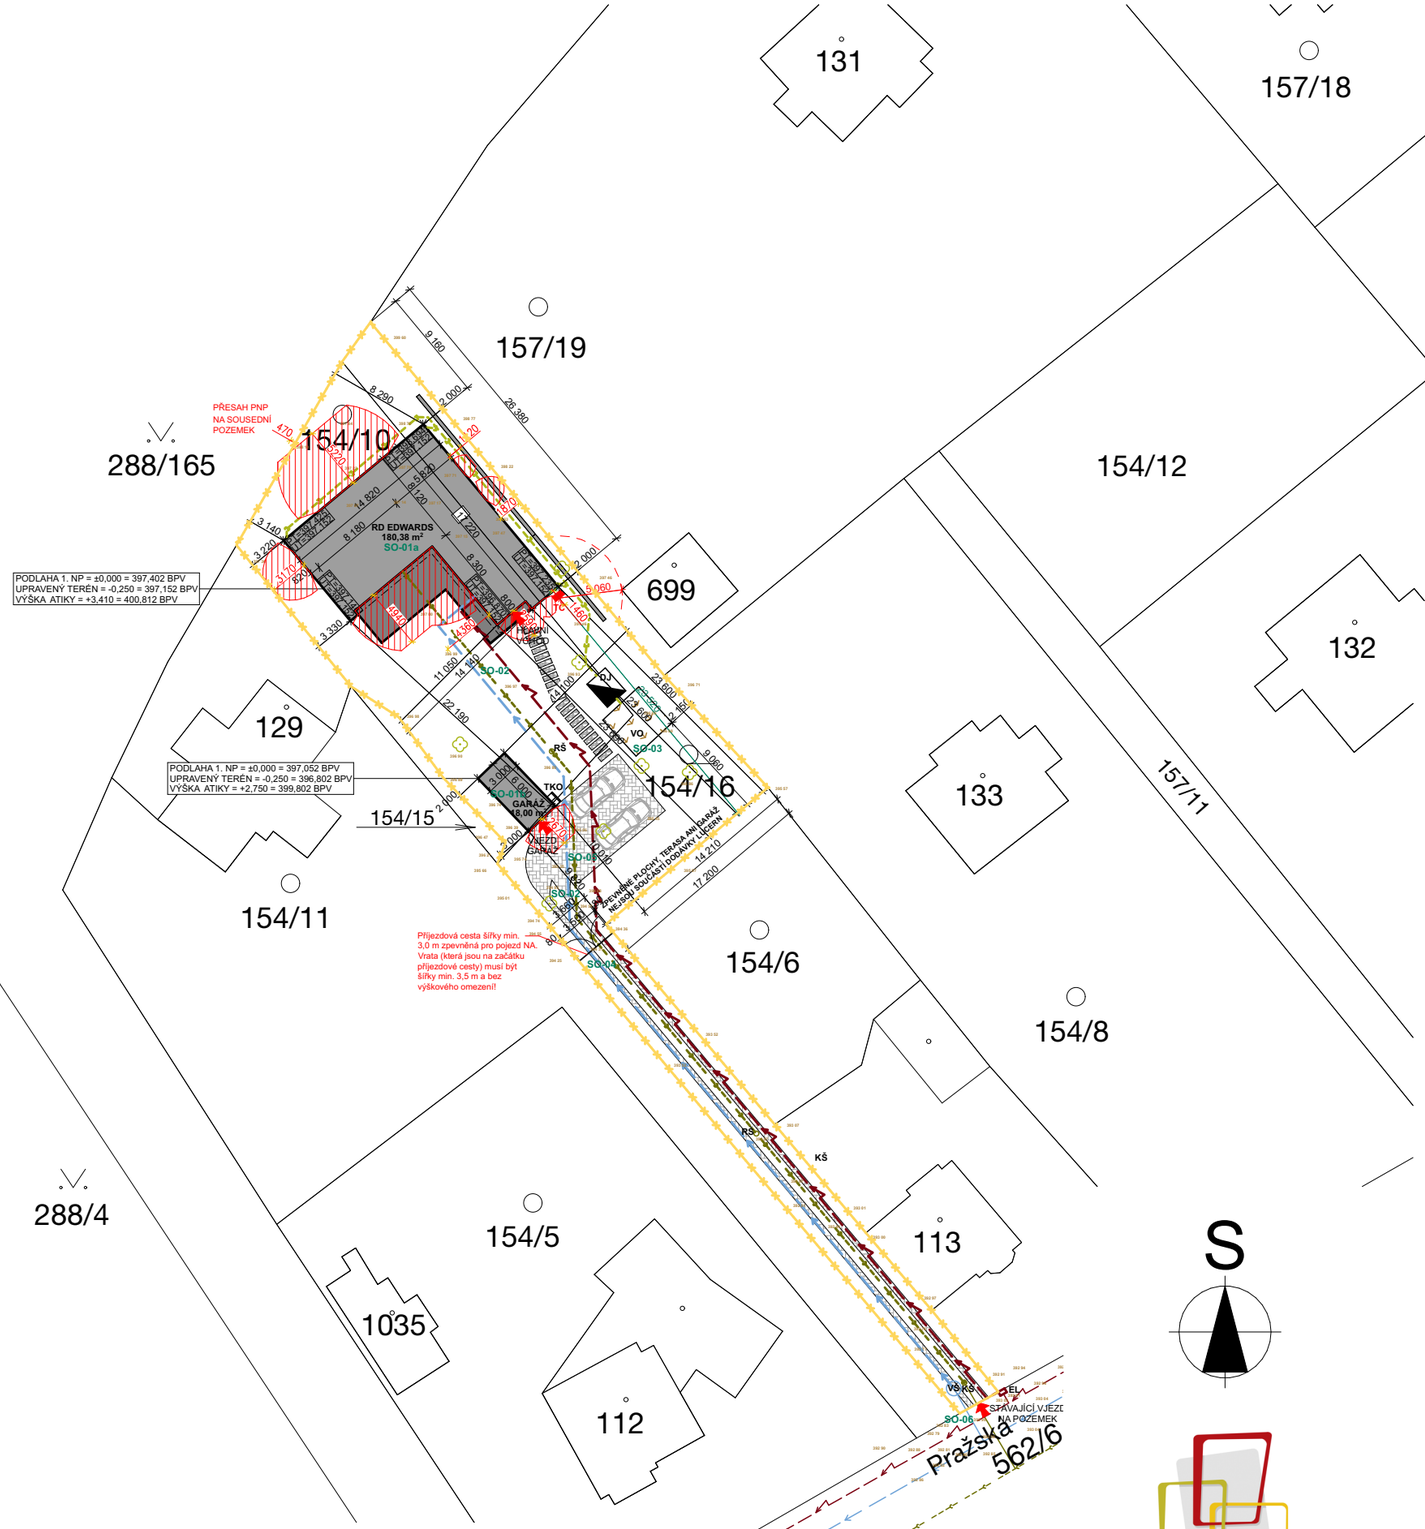

EL
ELEKTROMĚROVÁ SKŘÍŇ

TČ
TEPELNÉ ČERPADLO VZDUCH - VODA

TKO
TUHÝ KOMUNÁLNÍ ODPAD

KŠ
KANALIZAČNÍ ŠACHTA
⌀ DN 400, POJEZDOVÁ

VŠ
VODOVODNÍ ŠACHTA
⌀ DN 1 200, POJEZDOVÁ

DJ
DEŠŤOVÁ JÍMKA min. 5 m³

RŠ
REVIZNÍ ŠACHTA
⌀ DN 400, POJEZDOVÁ

VO
VSAKOVACÍ OBJEKT min. 16 m²
OBJEM VSAK. OBJEKTU min. 9,76 m³

ROZDĚLENÍ DO STAVEBNÍCH OBJEKTŮ
- SO-01a - RODINNÝ DŮM
- SO-01b - GARÁŽ
- SO-02 - VNITŘNÍ ČÁSTI PŘÍPOJEK
- SO-03 - LIKVIDACE DEŠŤOVÝCH VOD
- SO-04 - STÁVAJÍCÍ VJEZD NA POZEMEK
- SO-05 - ZPEVNĚNÉ PLOCHY, TERÉNNÍ ÚPRAVY
- SO-06 - ULIČNÍ OPLOCENÍ, BRÁNA, BRANKA

S

LUCERN
moderní dřevostavby

LUCERN DŘEVOSTAVBY s.r.o.
ÚDOLNÍ 280/15
PRAHA 4 - BRANÍK
147 00

± 0,000 = 397,402 m. n. m. (Bpv)

INVESTOR
Bc. Markéta Edwards,
K dálnici 167, Pitkovice,
104 00 Praha 10

STAVBA
NOVOSTAVBA RODINNÉHO DOMU
č. parc.: 154/10 a 154/16
k.ú.: Jevany [659312]

OBEC
Jevany [533378]

STUPEŇ PD
DSP + DPS

VEDOUCÍ PROJEKTU
Ing. Josef Frydrýn

VYPRACOVAL
Ing. Václav Křepelák, DiS.

AUTORIZACE
Ing. Miloš Slavík

DATUM
09/2025

MĚŘÍTKO
1:500

VÝKRES
SITUACE KOORDINAČNÍ

C.3.

Digitálně podepsal Ing. Miloš Slavík
Datum: 2026.03.09 08:44:29 +01'00'