ELEKTRO
NAPOJENÍ ELETŘINY BUDE PROVEDENO DO ELETROMĚROVÉ SKŘÍNĚ NA HRANICI POZEMKU.
ELEKTROMĚR JE OSAZEN U POZEMKU STAVEBNÍKA.
KANALIZACE
SPLAŠKOVÉ VODY BUDOU GRAVITAČNĚ SVÁDĚNY DO KANALIZAČNÍ ŠACHTY A NÁSLEDNĚ DO KANALIZAČNÍHO ŘADU.
VODA
NAPOJENÍ Z VODOVODNÍHO ŘADU PŘES VODOMĚRNOU ŠACHTU.

POZNÁMKY:

PLOCHA POZEMKU CELKEM:	1 091,00 m^2
ZASTAVĚNÁ PLOCHA RD:	180,38 m^2
ZPEVNĚNÉ PLOCHY, TERASA, GARÁŽ:	170,94 m^2
ZASTAVĚNOST POZEMKU:	15,67 %
ZBYLÁ ZELENÁ PLOCHA POZEMKU:	84,33 %

LEGENDA:
- HRANICE POZEMKU DLE KN
- STÁVAJÍCÍ VEDENÍ NÍZKÉHO NAPĚTÍ DO 1 kV
- STÁVAJÍCÍ PŘÍPOJKA DO ELEKTRO PILÍŘE 0,84 m
- NAVRŽENÁ DOMOVNÍ PŘÍPOJKA ELEKTRA 82,15 m
- STÁVAJÍCÍ PŘÍPOJKA SPLAŠKOVÉ KANALIZACE 8,15 m
- NAVRŽENÁ DOMOVNÍ PŘÍPOJKA SPLAŠKOVÉ KANALIZACE 39,91 m
- STÁVAJÍCÍ VEDENÍ VODOVODU
- STÁVAJÍCÍ PŘÍPOJKA VODOVODU 4,96 m
- NAVRŽENÁ DOMOVNÍ PŘÍPOJKA VODOVODU 80,97 m
- NAVRŽENÁ DOMOVNÍ PŘÍPOJKA DEŠŤOVÉ KANALIZACE 57,40 m
- OPLOCENÍ - HRANICE POZEMKU DLE KN - STÁVAJÍCÍ, DRÁTĚNÉ, S BETONOVÝMI SLOUPKY
- OPLOCENÍ ULIČNÍ - STÁVAJÍCÍ, DRÁTĚNÉ, S BETONOVÝMI SLOUPY
- POŽÁRNĚ NEBEZPEČNÝ PROSTOR OD FASÁDY OBJEKTU

SOUHLASY VLASTNÍKŮ SOUSEDNÍCH POZEMKŮ

TENTO SOUHLAS BUDE PŘEDLOŽEN K ŽÁDOSTI O ÚZEMNÍ SOUHLAS DLE § 96 ODST. 3, PÍSM. d), ZÁKON Č. 283/2021 Sb. (STAVEBNÍ ZÁKON) A K ŽÁDOSTI O OHLÁŠENÍ PODLE § 105 ODST. 1, PÍSM. f) ZÁKONA Č. 283/2021 Sb. (STAVEBNÍ ZÁKON).

TÍMTO DOKLADEM STAVEBNÍK PROKAZUJE, ŽE INFORMOVAL UVEDENÉ OSOBY A ORGÁNY O SVÉM ZÁMĚRU STAVBY RODINNÉHO DOMU NA PARCELE Č. 154/10 A 154/16, V K.Ú. JEVANY.

UVEDENÉ OSOBY A ORGÁNY POTVRZUJÍ SVÝM PODPISEM A DATEM, ŽE JSOU SEZNÁMENI A SOUHLASÍ SE ZÁMĚREM, JEHO SITUAČNÍM UMÍSTĚNÍM, VZHLEDEM NA ROZMĚRY, ODSTUPOVÉ VZDÁLENOSTI OD HRANIC POZEMKŮ.

VYJÁDŘENÍ VLASTNÍKŮ OKOLNÍCH NEMOVITOSTÍ

PARC. Č.	VLASTNÍK	DATUM NAROZENÍ/VZNIKU	DATUM PODPISU	PODPIS
st. 113	Hraníková Daniela, Ve Skále 727, 250 92 Šestajovice			
154/6	Hraníková Daniela, Ve Skále 727, 250 92 Šestajovice			
154/8	Skořepová Lucie, Nechvílova 1838/15, Chodov, 148 00 Praha 4			
157/19	Dušková Dagmar Ing., Hájecká 184, 253 03 Chýně			
562/6	Středočeský kraj, Zborovská 81/11, Smíchov, 150 00 Praha 5			
st. 129	Paul Oldřich MUDr., Högerova 1098/11, Hlubočepy, 152 00 Praha 5			
154/11	Paul Oldřich MUDr., Högerova 1098/11, Hlubočepy, 152 00 Praha 5			
154/15	Paul Oldřich MUDr., Högerova 1098/11, Hlubočepy, 152 00 Praha 5			
288/165	Tavandzis Georgios, Ježník 2433/104, Pod Bezručovým vrchem, 794 01 Krnov			

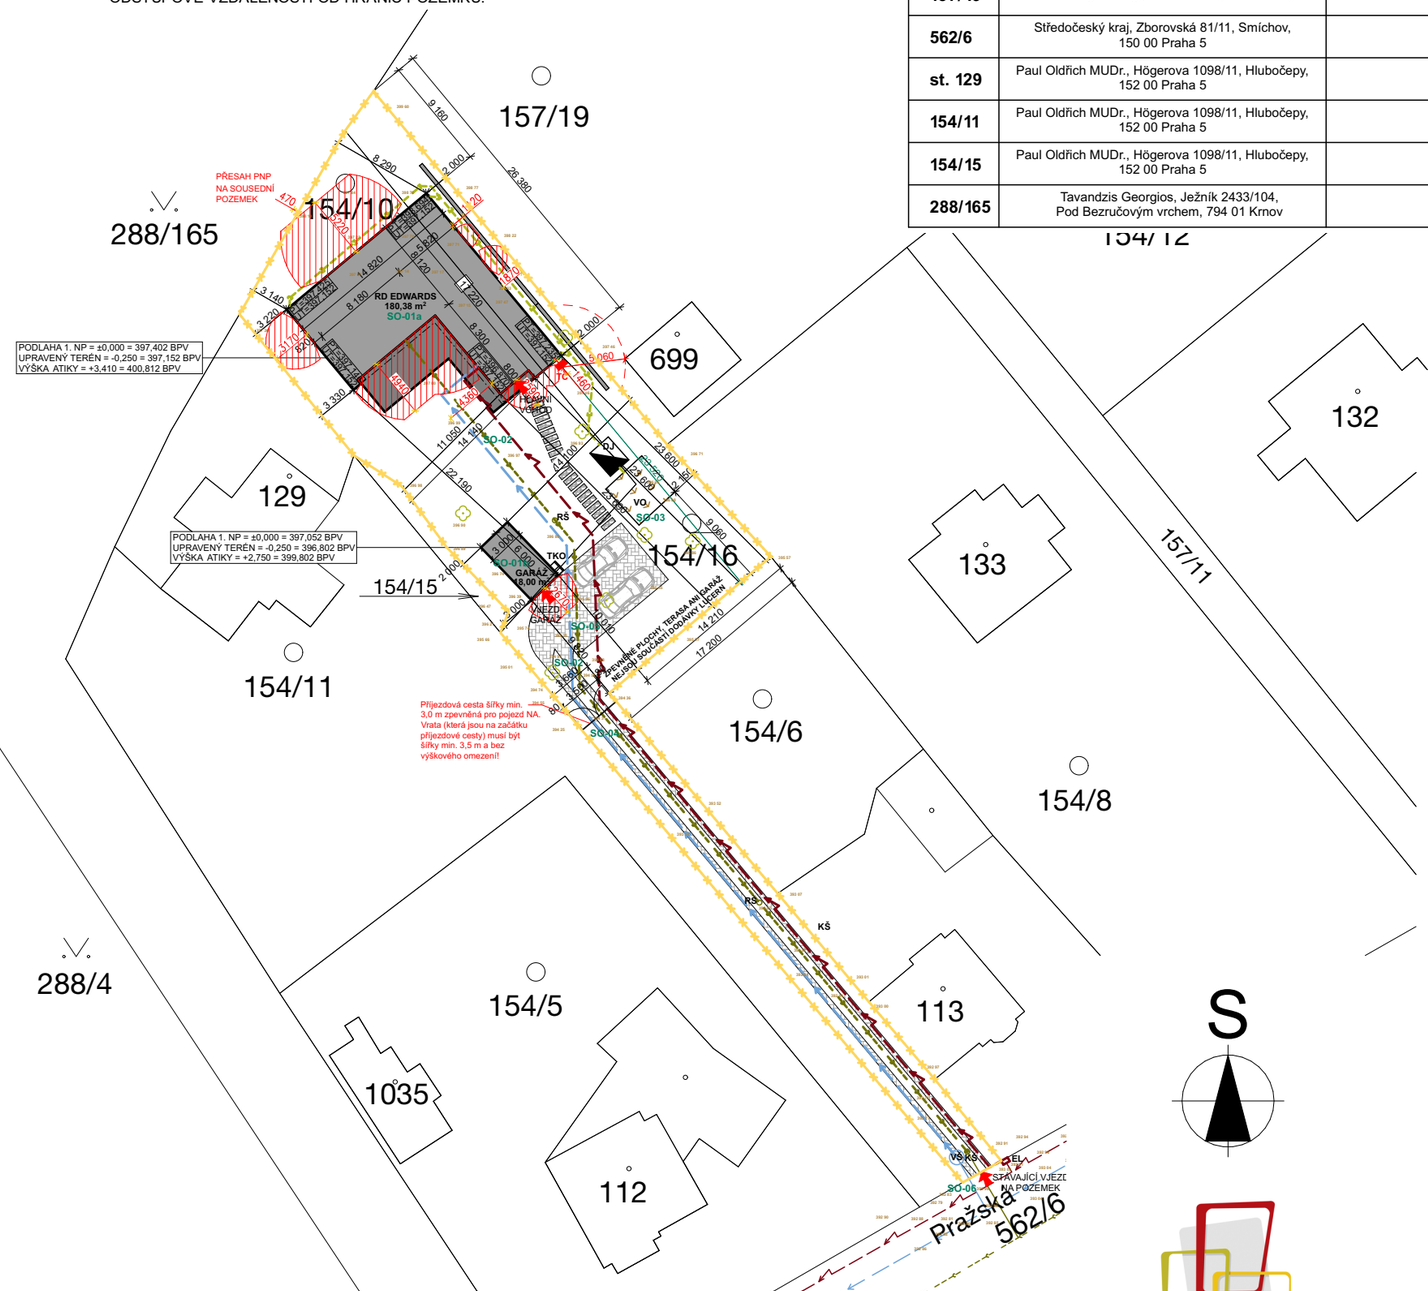

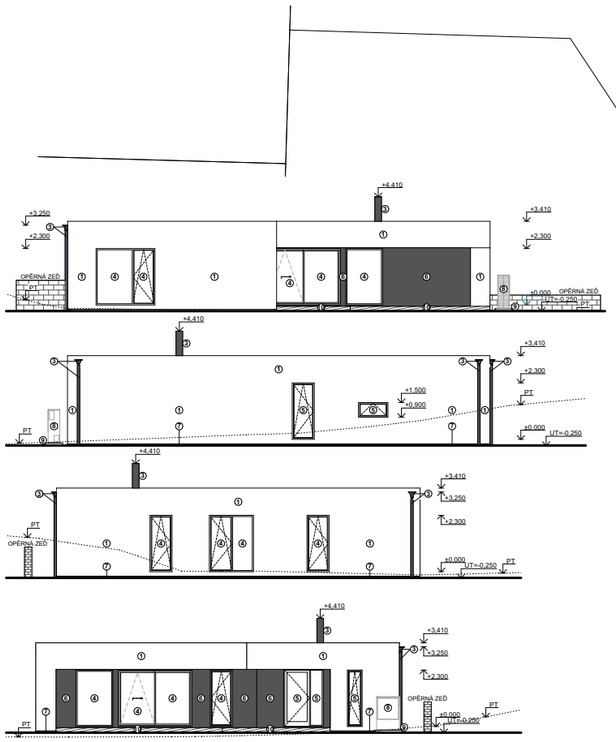

EL
ELEKTROMĚROVÁ SKŘÍŇ

TČ
TEPELNÉ ČERPADLO VZDUCH - VODA

TKO
TUHÝ KOMUNÁLNÍ ODPAD

KŠ
KANALIZAČNÍ ŠACHTA ⌀ DN 400, POJEZDOVÁ

VŠ
VODOVODNÍ ŠACHTA ⌀ DN 1 200, POJEZDOVÁ

DJ
DEŠŤOVÁ JÍMKA min. 5 m^3

RŠ
REVIZNÍ ŠACHTA ⌀ DN 400, POJEZDOVÁ

VO
VSAKOVACÍ OBJEKT min. 16 m^2
OBJEM VSAK. OBJEKTU min. 9,76 m^3

ROZDĚLENÍ DO STAVEBNÍCH OBJEKTŮ
- SO-01a - RODINNÝ DŮM
- SO-01b - GARÁŽ
- SO-02 - VNITŘNÍ ČÁSTI PŘÍPOJEK
- SO-03 - LIKVIDACE DEŠŤOVÝCH VOD
- SO-04 - STÁVAJÍCÍ VJEZD NA POZEMEK
- SO-05 - ZPEVNĚNÉ PLOCHY, TERÉNNÍ ÚPRAVY
- SO-06 - ULIČNÍ OPLOCENÍ, BRÁNA, BRANKA

LUCERN
moderní dřevostavby

LUCERN DŘEVOSTAVBY s.r.o.
ÚDOLNÍ 280/15
PRAHA 4 - BRANÍK
147 00

± 0,000 = 397,402 m. n. m. (Bpv)

INVESTOR
Bc. Markéta Edwards,
K dálnici 167, Pitkovice,
104 00 Praha 10

STAVBA
NOVOSTAVBA RODINNÉHO DOMU
č. parc.: 154/10 a 154/16
k.ú.: Jevany [659312]

OBEC
Jevany [533378]

STUPEŇ PD
DSP + DPS

VEDOUCÍ PROJEKTU
Ing. Josef Frydrýn

VYPRACOVAL
Ing. Václav Křepelák, DiS.

AUTORIZACE
Ing. Miloš Slavík

DATUM
09/2025

MĚŘÍTKO
1:500

VÝKRES
SITUACE PODPISOVÁ

C.4.

Ing. MILOŠ SLAVÍK
Autorizovaný inženýr pro pozemní stavby
ČKAIT - 0010081

Digitálně podepsal Ing. Miloš Slavík
Datum: 2026.03.09 08:44:03 +01'00'