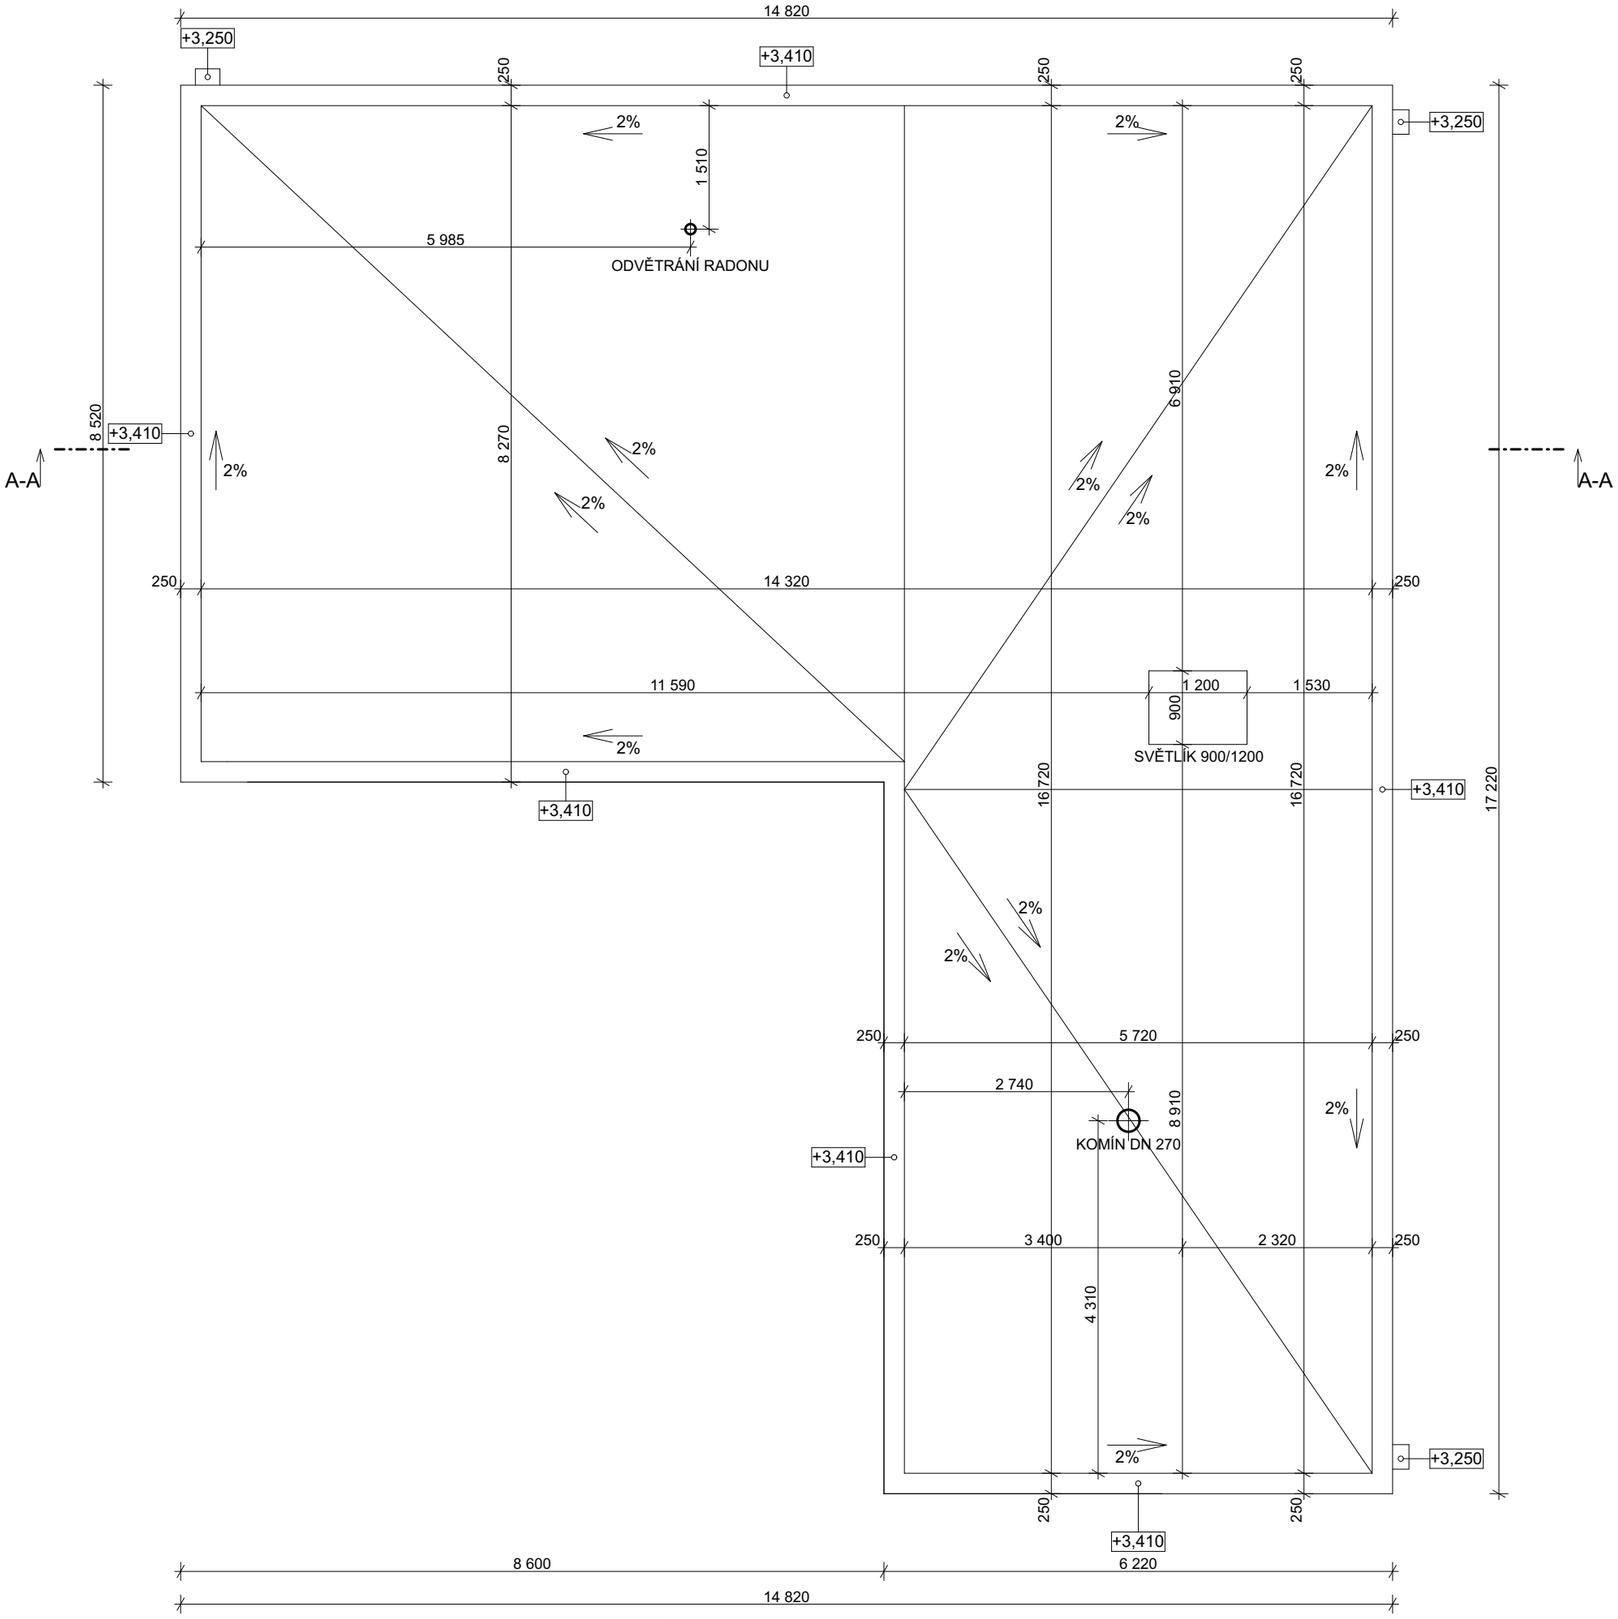

LEGENDA MATERIÁLŮ			
OZNAČENÍ	POPIS MATERIÁLU	OZNAČENÍ	POPIS MATERIÁLU
	TEPELNÁ IZOLACE MINERÁLNÍ VATA/EPS		DŘEVO
	TEPELNÁ IZOLACE XPS		ZEMINA PŮVODNÍ
	BETON PROSTÝ		ZEMINA NASYPANÁ
	BETON VYZTUŽENÝ		ŠTĚRK
	BETONOVÉ TVÁRNICE NOSNÉ		HYDROIZOLACE

- PŘI PROVÁDĚNÍ VEŠKERÝCH KONSTRUKCÍ JE NUTNO DODRŽET TECHNOLOGICKÉ POSTUPY JEDNOTLIVÝCH VÝROBCŮ.
- VŠECHNY KONSTRUKCE JSOU KÓTOVÁNY SKLADEBNĚ.
- VŠECHNA VÝROBNÍ DOKUMENTACE MUSÍ BÝT ODSOUHLASENA PROJEKTANTEM.
- STROPNÍ TRÁMY SPOJENY S POZEDNICÍ SVRONÍKY NEBO SYSTÉMOVÝMI PRVKY BOVA.
- STŘEŠNÍ KRYTINA BUDE PROVEDENA Z PVC FOLIE, VČETNĚ VEŠKERÝCH DOPLŇKŮ, ODSTÍN BUDE UPRAVEN PODLE POŽADAVKŮ STAVEBNÍKA.
- VEŠKERÉ STAVEBNÍ PRÁCE NUTNO PROVÁDĚT PODLE PRACOVNÍCH, TECHNOLOGICKÝCH A TECHNICKÝCH PŘEDPISŮ A PŘÍSLUŠNÝCH DOPORUČENÍ VÝROBCŮ JEDNOTLIVÝCH STAVEBNÍCH SYSTÉMŮ.

Digitálně podepsal Ing. Miloš Slavík
Datum: 2026.03.09 08:53:05 +01'00'

Ing. MILOŠ SLAVÍK
Autorizovaný inženýr pro pozemní stavby
ČKAIT - 0012081

LUCERN
moderní dřevostavby

LUCERN DŘEVOSTAVBY s.r.o.
ÚDOLNÍ 280/15
PRAHA 4 - BRANÍK
147 00

± 0,000 = 397,402 m. n. m. (Bpv)

INVESTOR
Bc. Markéta Edwards,
K dálnici 167, Pitkovice,
104 00 Praha 10

STAVBA
NOVOSTAVBA RODINNÉHO DOMU
č. parc.: 154/10 a 154/16
k.ú.: Jevany [659312]

OBEC
Jevany [533378]

STUPEŇ PD
DSP + DPS

VEDOUCÍ PROJEKTU
Ing. Josef Frydrýn

VYPRACOVAL
Ing. Václav Křepelák, DiS.

AUTORIZACE
Ing. Miloš Slavík

DATUM
09/2025

MĚŘÍTKO
1:75

VÝKRES
PŮDORYS STŘECHY

D.1.1.4.