W1 - SKLADBA VNITŘNÍ NOSNÉ STĚNY	
DESKA RIGISTABIL	12,5 mm
KVH HRANOLY 60/120 + MINERÁLNÍ IZOLACE	120 mm
DESKA RIGISTABIL	12,5 mm

W6 - SKLADBA OBVODOVÉ STĚNY LUCERN EKO PLUS	
SILIKONOVÁ FASÁDA, TOČENÁ, ZRNO 1,5	1,5 mm
PENETRACE	
STĚRKOVÉ LEPIDLO, VČ. ARMOVACÍ TKANINY	3,5 mm
IZOLACE EPS 70 F	160 mm
LEPÍCÍ TMEL	5 mm
DESKA RIGISTABIL	15 mm
KVH HRANOLY 60/120 + MINERÁLNÍ IZOLACE	120 mm
PAROTĚSNÁ ZÁBRANA FOLIE PE 190 g/m^2	
DŘEVĚNÝ ROŠT 40/60 + MINERÁLNÍ IZOLACE	40 mm
DESKA RIGISTABIL	12,5 mm

W7 - SKLADBA ATIKY LUCERN EKO PLUS	
SILIKONOVÁ FASÁDA, TOČENÁ, ZRNO 1,5	1,5 mm
PENETRACE	
STĚRKOVÉ LEPIDLO, VČ. ARMOVACÍ TKANINY	3,5 mm
IZOLACE EPS 70 F	160 mm
LEPÍCÍ TMEL	5 mm
OSB DESKA	25 mm
TEPELNÁ IZOLACE EPS 70 F	60 mm

P2 – SKLADBA PODLAHY 1. NP – DŘEVĚNÁ PODLAHA	
DŘEVĚNÁ VRSTVENÁ KRYTINA	11 mm
BETONOVÝ POTĚR HLAZENÝ	63 mm
SYSTÉMOVÁ DESKA PODLAHOVÉHO VYTÁPĚNÍ	2 mm
PE FOLIE	
TEPELNÁ IZOLACE EPS 100 Z	100 mm
HYDROIZOLACE – ASFALTOVÝ PÁS	4 mm
PODKLADNÍ BETONOVÁ MAZANINA, VČETNĚ	
SÍTÍ KARI 5/150/150 150 mm	150 mm
ŠTĚRKOPÍSKOVÝ NÁSYP	100 mm
PŮVODNÍ ZEMINA	

S1 - SKLADBA STŘECHY PLOCHÉ	
PVC FÓLIE	1,5 mm
GEOTEXTÍLIE min. 200 g/m^2	
SPÁDOVÉ KLÍNY Z EPS 100 S STABIL	20-180 mm
TEPELNÁ IZOLACE EPS 100 S STABIL	220 mm
POJISTNÁ HYDROIZOLACE	
OSB P+D	25 mm
STROPNÍ TRÁMY 80/220	220 mm
PAROTĚSNÁ FOLIE PE 190 g/m^2	
SNÍŽENÝ SDK PODHLED NA DŘEVĚNOU KONSTRUKCI	
Z KVH HRANOLŮ 40/60 Z TLOUŠŤKY 12,5 mm	115-415 mm

LEGENDA MATERIÁLŮ			
OZNAČENÍ	POPIS MATERIÁLU	OZNAČENÍ	POPIS MATERIÁLU
	TEPELNÁ IZOLACE MINERÁLNÍ VATA/EPS		DŘEVO
	TEPELNÁ IZOLACE XPS		ZEMINA PŮVODNÍ
	BETON PROSTÝ		ZEMINA NASYPANÁ
	BETON VYZTUŽENÝ		ŠTĚRK
	BETONOVÉ TVÁRNICE NOSNÉ		HYDROIZOLACE

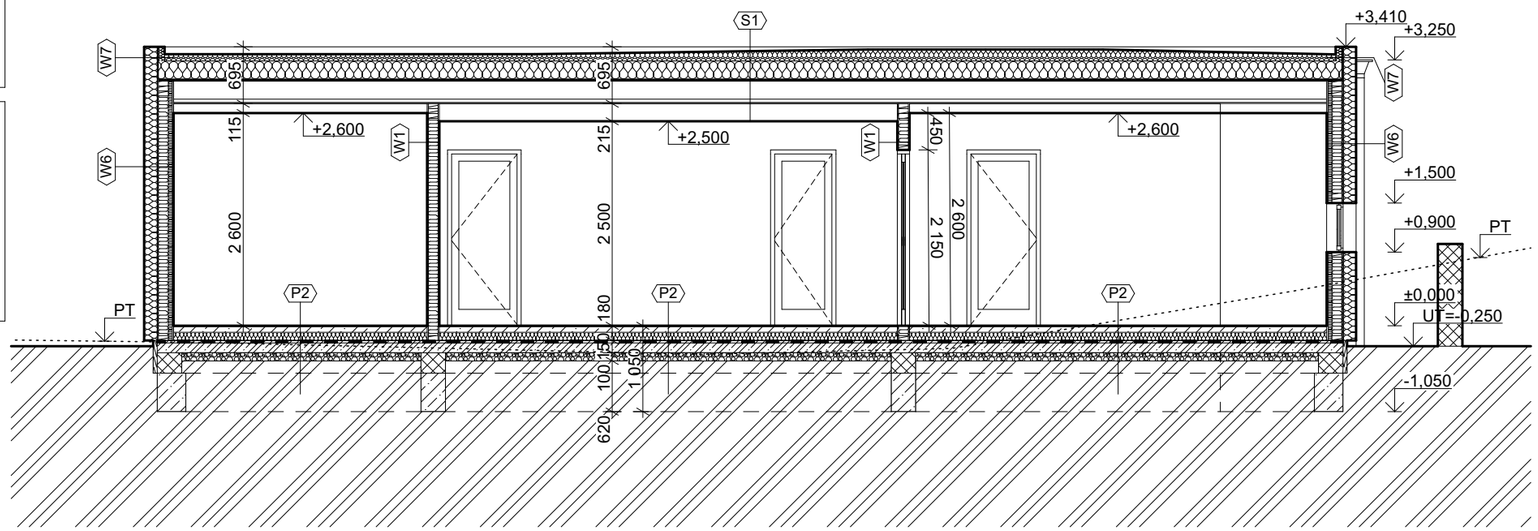

± 0,000 = 397,402 m. n. m. (Bpv)

- PŘI PROVÁDĚNÍ VEŠKERÝCH KONSTRUKCÍ JE NUTNO DODRŽET TECHNOLOGICKÉ POSTUPY JEDNOTLIVÝCH VÝROBCŮ.
- PODLAHOVÉ KONSTRUKCE BUDOU DILATOVÁNY PODLE PŘEDPISŮ VÝROBCE.
- VŠECHNY KONSTRUKCE JSOU KÓTOVÁNY SKLADEBNĚ.
- VŠECHNA VÝROBNÍ DOKUMENTACE MUSÍ BÝT ODSOUHLASENA PROJEKTANTEM.
- V MÍSTNOSTEH S VLHKÝM PROVOZEM MUSÍ BÝT POUŽITY IMPREGNOVANÉ SDK DESKY NEBO RIGIDUROVÉ DESKY.
- STROPNÍ TRÁMY SPOJENY S POZEDNICÍ SVRONÍKY NEBO SYSTÉMOVÝMI PRVKY BOVA.
- VE ŠTĚRKOVÉM LOŽI POD ZÁKLADOVOU DESKOU BUDE PROVEDEN ROZVOD DRENÁŽNÍCH TRUBEK DN 60 PRO PŘÍPADNÉ ODVĚTRÁNÍ RADONU Z PODLOŽÍ. VYÚSTĚNÍ BUDE PROVEDENO NAD STŘECHU V SDK PŘEDSTĚNĚ.
- ZÁKLADOVÉ PASY BUDOU PROVEDENY Z BETONU C 16/20 - XC 2.
- PŘI VÝSKYTU SPODNÍ VODY V ZÁKLADOVÉ SPÁŘE JE NUTNO PŘEHODNOTIT ZAKLÁDÁNÍ STAVBY A MATERIÁLY PRO IZOLACE.
- STŘEŠNÍ KRYTINA BUDE PROVEDENA Z PVC FOLIE, VČETNĚ VEŠKERÝCH DOPLŇKŮ, ODSTÍN BUDE UPRAVEN PODLE POŽADAVKŮ STAVEBNÍKA.
- VEŠKERÉ STAVEBNÍ PRÁCE NUTNO PROVÁDĚT PODLE PRACOVNÍCH, TECHNOLOGICKÝCH A TECHNICKÝCH PŘEDPISŮ A PŘÍSLUŠNÝCH DOPORUČENÍ VÝROBCŮ JEDNOTLIVÝCH STAVEBNÍCH SYSTÉMŮ.

Digitálně podepsal Ing. Miloš Slavík
Datum: 2026.03.09 08:52:43 +01'00'

LUCERN
moderní dřevostavby

LUCERN DŘEVOSTAVBY s.r.o.
ÚDOLNÍ 280/15
PRAHA 4 - BRANÍK
147 00

INVESTOR
Bc. Markéta Edwards,
K dálnici 167, Pitkovice,
104 00 Praha 10

STAVBA
NOVOSTAVBA RODINNÉHO DOMU
č. parc.: 154/10 a 154/16
k.ú.: Jevany [659312]

OBEC
Jevany [533378]

STUPEŇ PD
DSP + DPS

VEDOUCÍ PROJEKTU
Ing. Josef Frydrýn

VYPRACOVAL
Ing. Václav Křepelák, DiS.

AUTORIZACE
Ing. Miloš Slavík

DATUM
09/2025

MĚŘÍTKO
1:75

VÝKRES
ŘEZ A-A

D.1.1.5.