POHLED VÝCHODNÍ

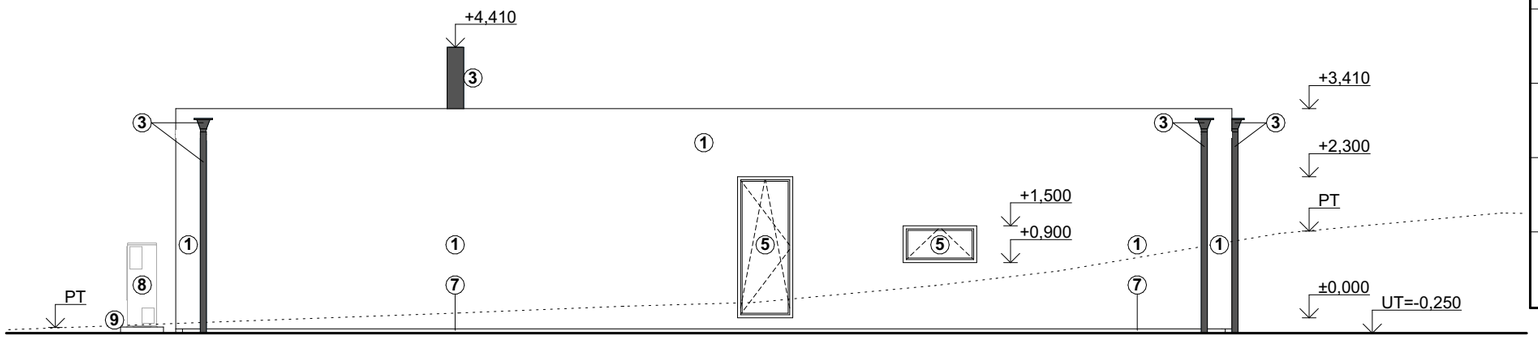

LEGENDA MATERIÁLŮ			
OZNAČENÍ	POPIS MATERIÁLU	OZNAČENÍ	POPIS MATERIÁLU
	TEPELNÁ IZOLACE MINERÁLNÍ VATA/EPS		DŘEVO
	TEPELNÁ IZOLACE XPS		ZEMINA PŮVODNÍ
	BETON PROSTÝ		ZEMINA NASYPANÁ
	BETON VYZTUŽENÝ		ŠTĚRK
	BETONOVÉ TVÁRNICE NOSNÉ		HYDROIZOLACE

POHLED ZÁPADNÍ

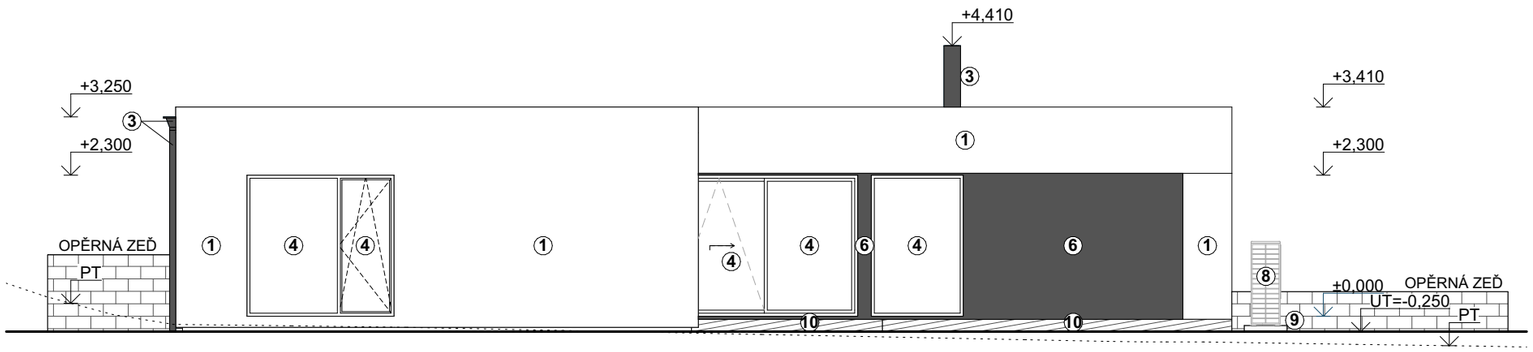

± 0,000 = 397,402 m. n. m. (Bpv)

INVESTOR

Bc. Markéta Edwards,
K dálnici 167, Pitkovice,
104 00 Praha 10

STAVBA

NOVOSTAVBA RODINNÉHO DOMU
č. parc.: 154/10 a 154/16
k.ú.: Jevany [659312]

OBEC

Jevany [533378]

STUPEŇ PD

DSP + DPS

VEDOUCÍ PROJEKTU

Ing. Josef Frydrýn

VYPRACOVAL

Ing. Václav Křepelák, DiS.

AUTORIZACE

Ing. Miloš Slavík

DATUM

09/2025

MĚŘÍTKO

1:100

VÝKRES

POHLED VÝCHODNÍ/ZÁPADNÍ

D.1.1.7.

PĚRNÁ ZEĎ NENÍ SOUČÁSTÍ DODÁVKY LUCERN

LEGENDA POVRCHOVÝCH ÚPRAV	
1	SILIKONOVÁ OMÍTKA ZRNITOST 1,5 - BÍLÁ BARVA
2	PVC FOLIE
3	KLEMPÍŘSKÉ A KOVOVÉ PRVKY (ODSTÍN PODLE POŽADAVKŮ STAVEBNÍKA)
4	VÝPLNĚ OTVORŮ (ODSTÍN PODLE POŽADAVKŮ STAVEBNÍKA) - ČIRÉ ZASKLENÍ
5	VÝPLNĚ OTVORŮ (ODSTÍN PODLE POŽADAVKŮ STAVEBNÍKA) - MLÉČNÉ ZASKLENÍ
6	SILIKONOVÁ OMÍTKA ZRNITOST 1,5 - ANTRACITOVÁ BARVA
7	ZATEPLENÍ SOKLU - XPS
8	TEPELNÉ ČERPADLO VZDUCH - VODA
9	BETON PROSTÝ
10	TERASOVÁ PRKNA

- PŘI PROVÁDĚNÍ VEŠKERÝCH KONSTRUKCÍ JE NUTNO DODRŽET TECHNOLOGICKÉ POSTUPY JEDNOTLIVÝCH VÝROBCŮ.
- VŠECHNA VÝROBNÍ DOKUMENTACE MUSÍ BÝT ODSOUHLASENA PROJEKTANTEM.
- STŘEŠNÍ KRYTINA BUDE PROVEDENA Z PVC FOLIE, VČETNĚ VEŠKERÝCH DOPLŇKŮ, ODSTÍN BUDE UPRAVEN PODLE POŽADAVKŮ STAVEBNÍKA.
- VEŠKERÉ STAVEBNÍ PRÁCE NUTNO PROVÁDĚT PODLE PRACOVNÍCH, TECHNOLOGICKÝCH A TECHNICKÝCH PŘEDPISŮ A PŘÍSLUŠNÝCH DOPORUČENÍ VÝROBCŮ JEDNOTLIVÝCH STAVEBNÍCH SYSTÉMŮ.

Ing. MILOŠ SLAVÍK
Autorizovaný inženýr pro pozemní stavby
ČKAIT - 0012081

Digitálně podepsal Ing. Miloš Slavík
Datum: 2026.03.09 08:51:54 +01'00'

LUCERN
moderní dřevostavby

LUCERN DŘEVOSTAVBY s.r.o.
ÚDOLNÍ 280/15
PRAHA 4 - BRANÍK
147 00