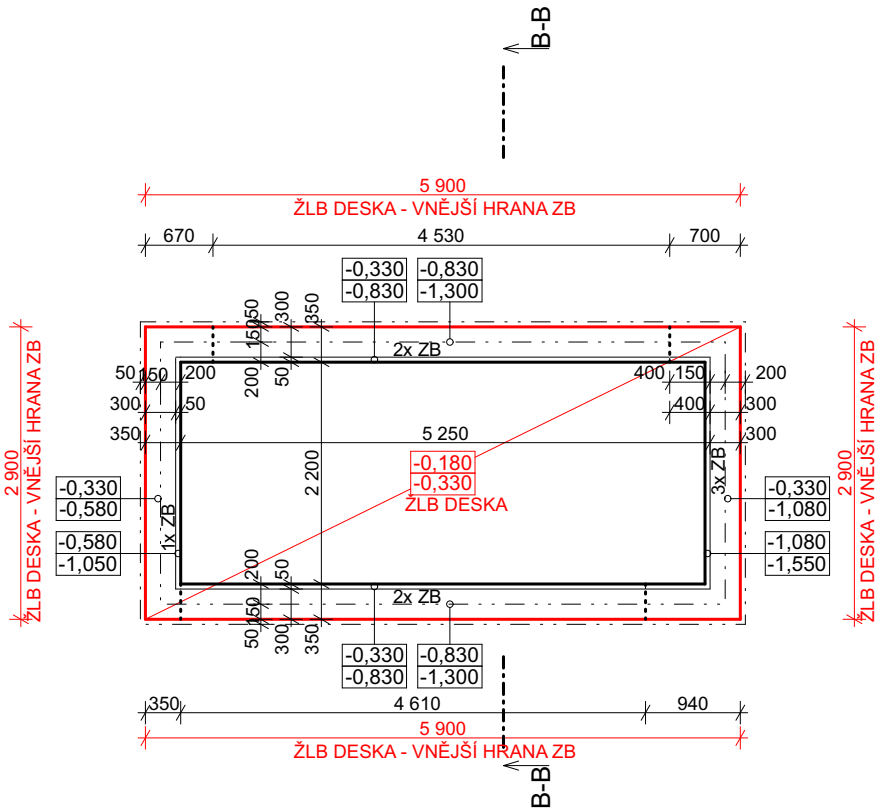

- PŘI PROVÁDĚNÍ VEŠKERÝCH KONSTRUKCÍ JE NUTNO DODRŽET TECHNOLOGICKÉ POSTUPY JEDNOTLIVÝCH VÝROBCŮ.
- VE ŠTĚRKOVÉM LOŽI POD ZÁKLADOVOU DESKOU BUDE PROVEDEN ROZVOD DRENÁŽNÍCH TRUBEK DN 60 PRO PŘÍPADNÉ ODVĚTRÁNÍ RADONU Z PODLOŽÍ. VYÚSTĚNÍ BUDE PROVEDENO SKRZ ZÁKLAD DO BOKU, KDE BUDE POTRUBÍ ZAVÍČKOVÁNO PRO PŘÍPADNÉ DOPOJENÍ VENKOVNÍHO ROZVODU.
- ZÁKLADOVÉ PASY BUDOU PROVEDENY Z BETONU C 16/20 - XC 2.
- PŘI VÝSKYTU SPODNÍ VODY V ZÁKLADOVÉ SPÁŘE JE NUTNO PŘEHODNOTIT ZAKLÁDÁNÍ STAVBY A MATERIÁLY PRO IZOLACE.
- VEŠKERÉ STAVEBNÍ PRÁCE NUTNO PROVÁDĚT PODLE PRACOVNÍCH, TECHNOLOGICKÝCH A TECHNICKÝCH PŘEDPISŮ A PŘÍSLUŠNÝCH DOPORUČENÍ VÝROBCŮ JEDNOTLIVÝCH STAVEBNÍCH SYSTÉMŮ.

LUCERN
moderní dřevostavby

LUCERN DŘEVOSTAVBY s.r.o.
ÚDOLNÍ 280/15
PRAHA 4 - BRANÍK
147 00

± 0,000 = 397,402 m. n. m. (Bpv)

INVESTOR

Bc. Markéta Edwards,
K dálnici 167, Pitkovice,
104 00 Praha 10

STAVBA

NOVOSTAVBA RODINNÉHO DOMU
č. parc.: 154/10 a 154/16
k.ú.: Jevany [659312]

OBEC

Jevany [533378]

STUPEŇ PD

DSP + DPS

VEDOUCÍ PROJEKTU

Ing. Josef Frydrýn

VYPRACOVAL

Ing. Václav Křepelák, DiS.

AUTORIZACE

Ing. Miloš Slavík

DATUM

09/2025

MĚŘÍTKO

1:75

VÝKRES

PŮDORYS ZÁKLADŮ GARÁŽE

D.1.1.8.

Digitálně podepsal Ing. Miloš Slavík
Datum: 2026.03.09 08:51:26 +01'00'