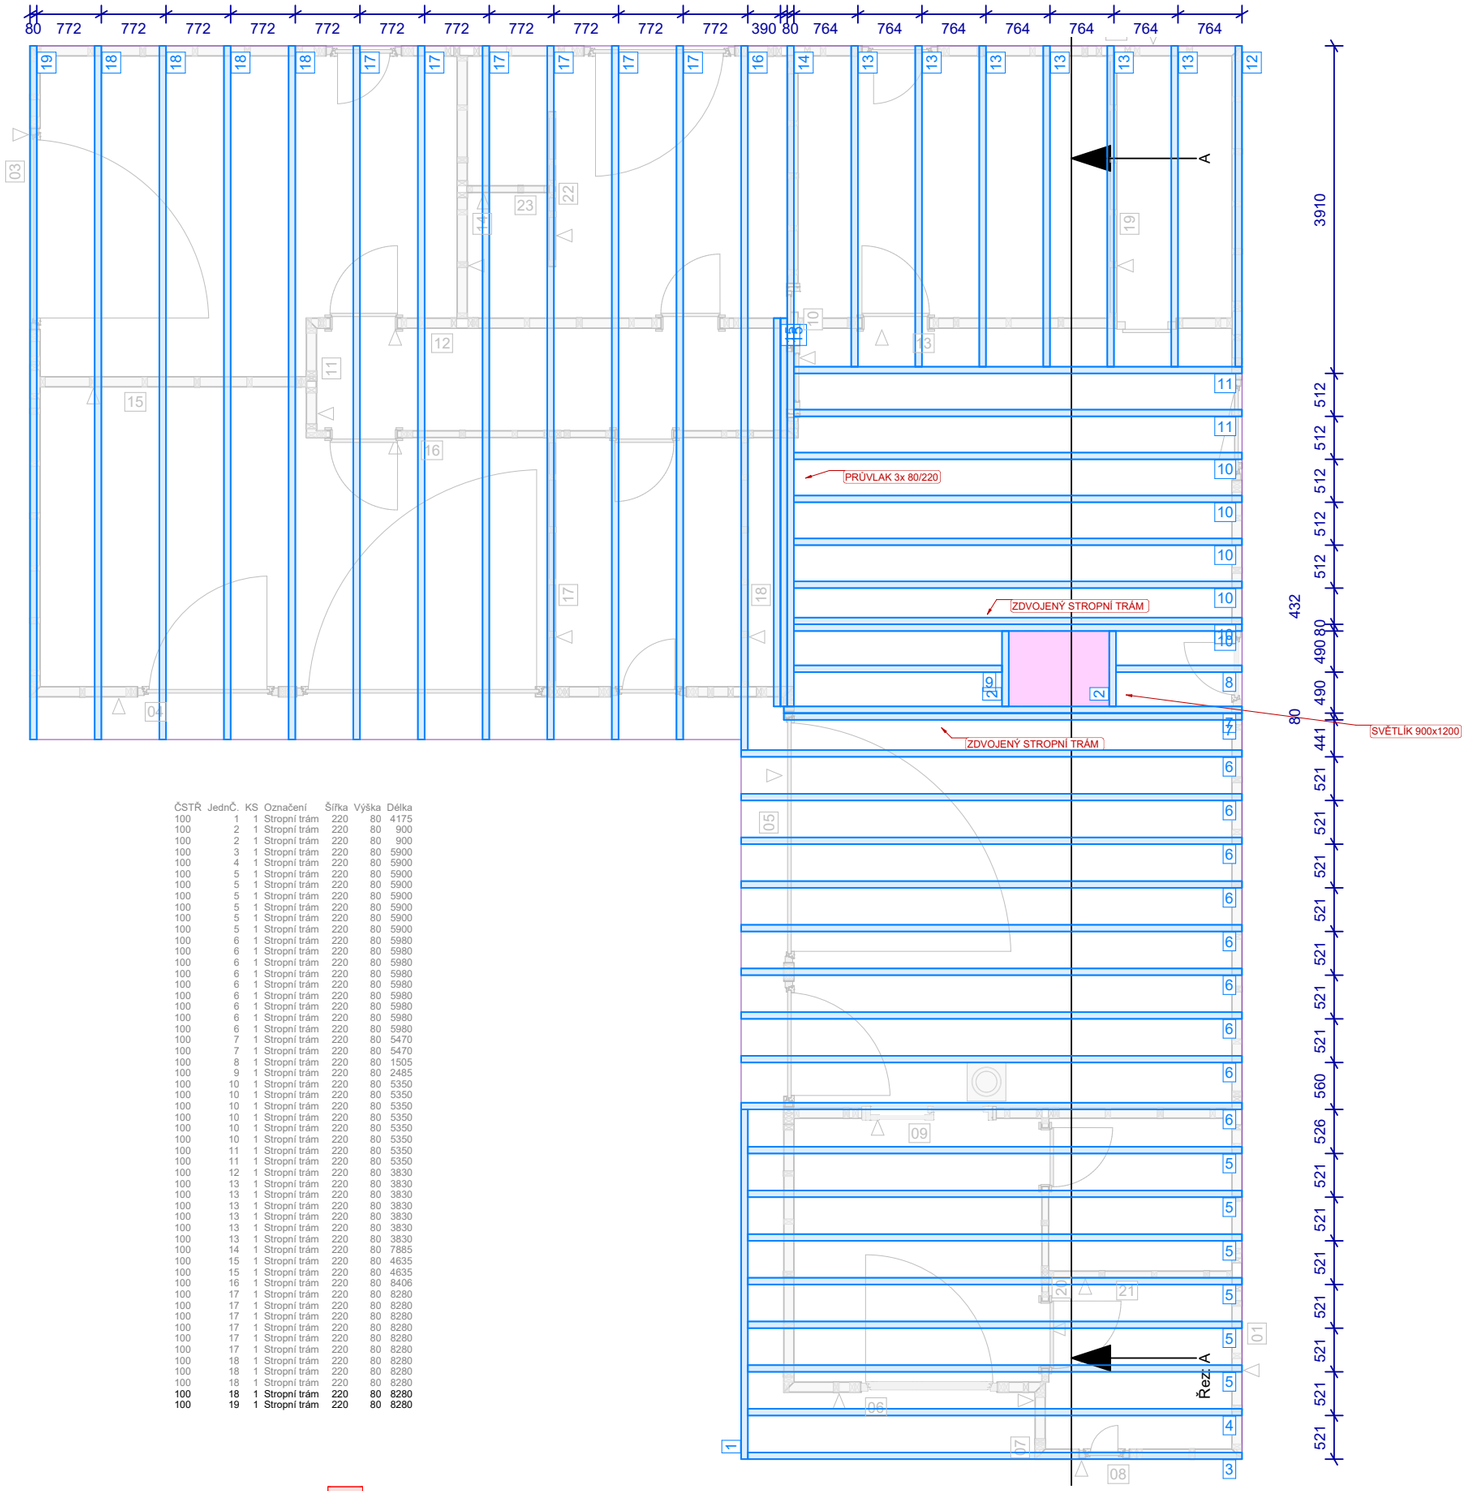

ČSTŘ	JednČ.	KS	Označení	Šířka	Výška	Délka
100	1	1	Stropní trám	220	80	4175
100	2	1	Stropní trám	220	80	900
100	2	1	Stropní trám	220	80	900
100	3	1	Stropní trám	220	80	5900
100	4	1	Stropní trám	220	80	5900
100	5	1	Stropní trám	220	80	5900
100	5	1	Stropní trám	220	80	5900
100	5	1	Stropní trám	220	80	5900
100	5	1	Stropní trám	220	80	5900
100	5	1	Stropní trám	220	80	5900
100	5	1	Stropní trám	220	80	5900
100	6	1	Stropní trám	220	80	5980
100	6	1	Stropní trám	220	80	5980
100	6	1	Stropní trám	220	80	5980
100	6	1	Stropní trám	220	80	5980
100	6	1	Stropní trám	220	80	5980
100	6	1	Stropní trám	220	80	5980
100	6	1	Stropní trám	220	80	5980
100	6	1	Stropní trám	220	80	5980
100	6	1	Stropní trám	220	80	5980
100	7	1	Stropní trám	220	80	5470
100	7	1	Stropní trám	220	80	5470
100	8	1	Stropní trám	220	80	1505
100	9	1	Stropní trám	220	80	2485
100	10	1	Stropní trám	220	80	5350
100	10	1	Stropní trám	220	80	5350
100	10	1	Stropní trám	220	80	5350
100	10	1	Stropní trám	220	80	5350
100	10	1	Stropní trám	220	80	5350
100	10	1	Stropní trám	220	80	5350
100	11	1	Stropní trám	220	80	5350
100	11	1	Stropní trám	220	80	5350
100	12	1	Stropní trám	220	80	3830
100	13	1	Stropní trám	220	80	3830
100	13	1	Stropní trám	220	80	3830
100	13	1	Stropní trám	220	80	3830
100	13	1	Stropní trám	220	80	3830
100	13	1	Stropní trám	220	80	3830
100	13	1	Stropní trám	220	80	3830
100	14	1	Stropní trám	220	80	7885
100	15	1	Stropní trám	220	80	4635
100	15	1	Stropní trám	220	80	4635
100	16	1	Stropní trám	220	80	8406
100	17	1	Stropní trám	220	80	8280
100	17	1	Stropní trám	220	80	8280
100	17	1	Stropní trám	220	80	8280
100	17	1	Stropní trám	220	80	8280
100	17	1	Stropní trám	220	80	8280
100	17	1	Stropní trám	220	80	8280
100	18	1	Stropní trám	220	80	8280
100	18	1	Stropní trám	220	80	8280
100	18	1	Stropní trám	220	80	8280
100	18	1	Stropní trám	220	80	8280
100	19	1	Stropní trám	220	80	8280

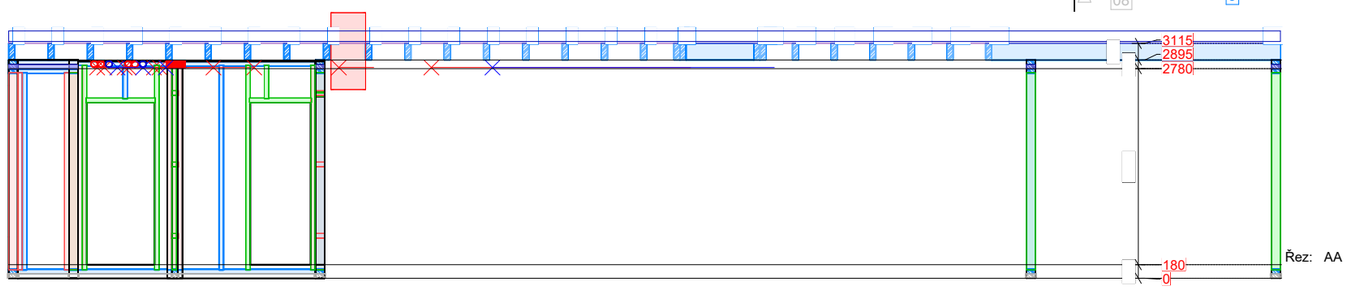

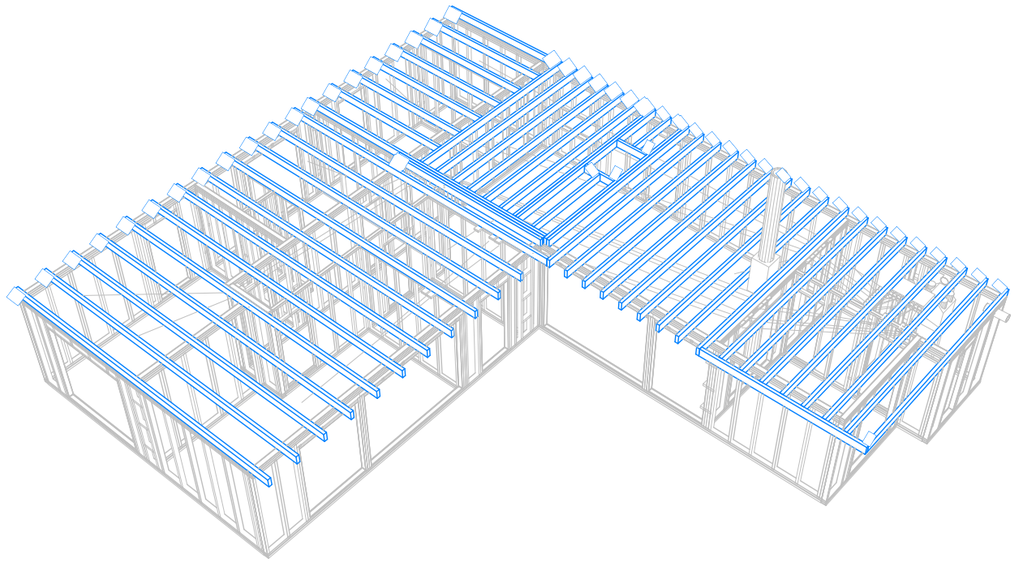

± 0,000 = 397,402 m. n. m. (Bpv)

INVESTOR

Bc. Markéta Edwards,
K dálnici 167, Pitkovice,
104 00 Praha 10

STAVBA

NOVOSTAVBA RODINNÉHO DOMU
č. parc.: 154/10 a 154/16
k.ú.: Jevany [659312]

OBEC

Jevany [533378]

STUPEŇ PD

DSP + DPS

VEDOUCÍ PROJEKTU

Ing. Josef Frydrýn

VYPRACOVAL

Ing. Petr Fait

AUTORIZACE

Ing. Miloš Slavík

Digitálně podepsal Ing. Miloš Slavík
Datum: 2026.03.09 08:55:23 +01'00'

Ing. MILOŠ SLAVÍK
Autorizovaný inženýr pro pozemní stavby
ČKAIT - 0012081

DATUM

09/2025

MĚŘÍTKO

1:75

VÝKRES

PŮDORYS A ŘEZ STROPEM

D.1.2.2.

LUCERN
moderní dřevostavby

LUCERN DŘEVOSTAVBY s.r.o.
ÚDOLNÍ 280/15
PRAHA 4 - BRANÍK
147 00