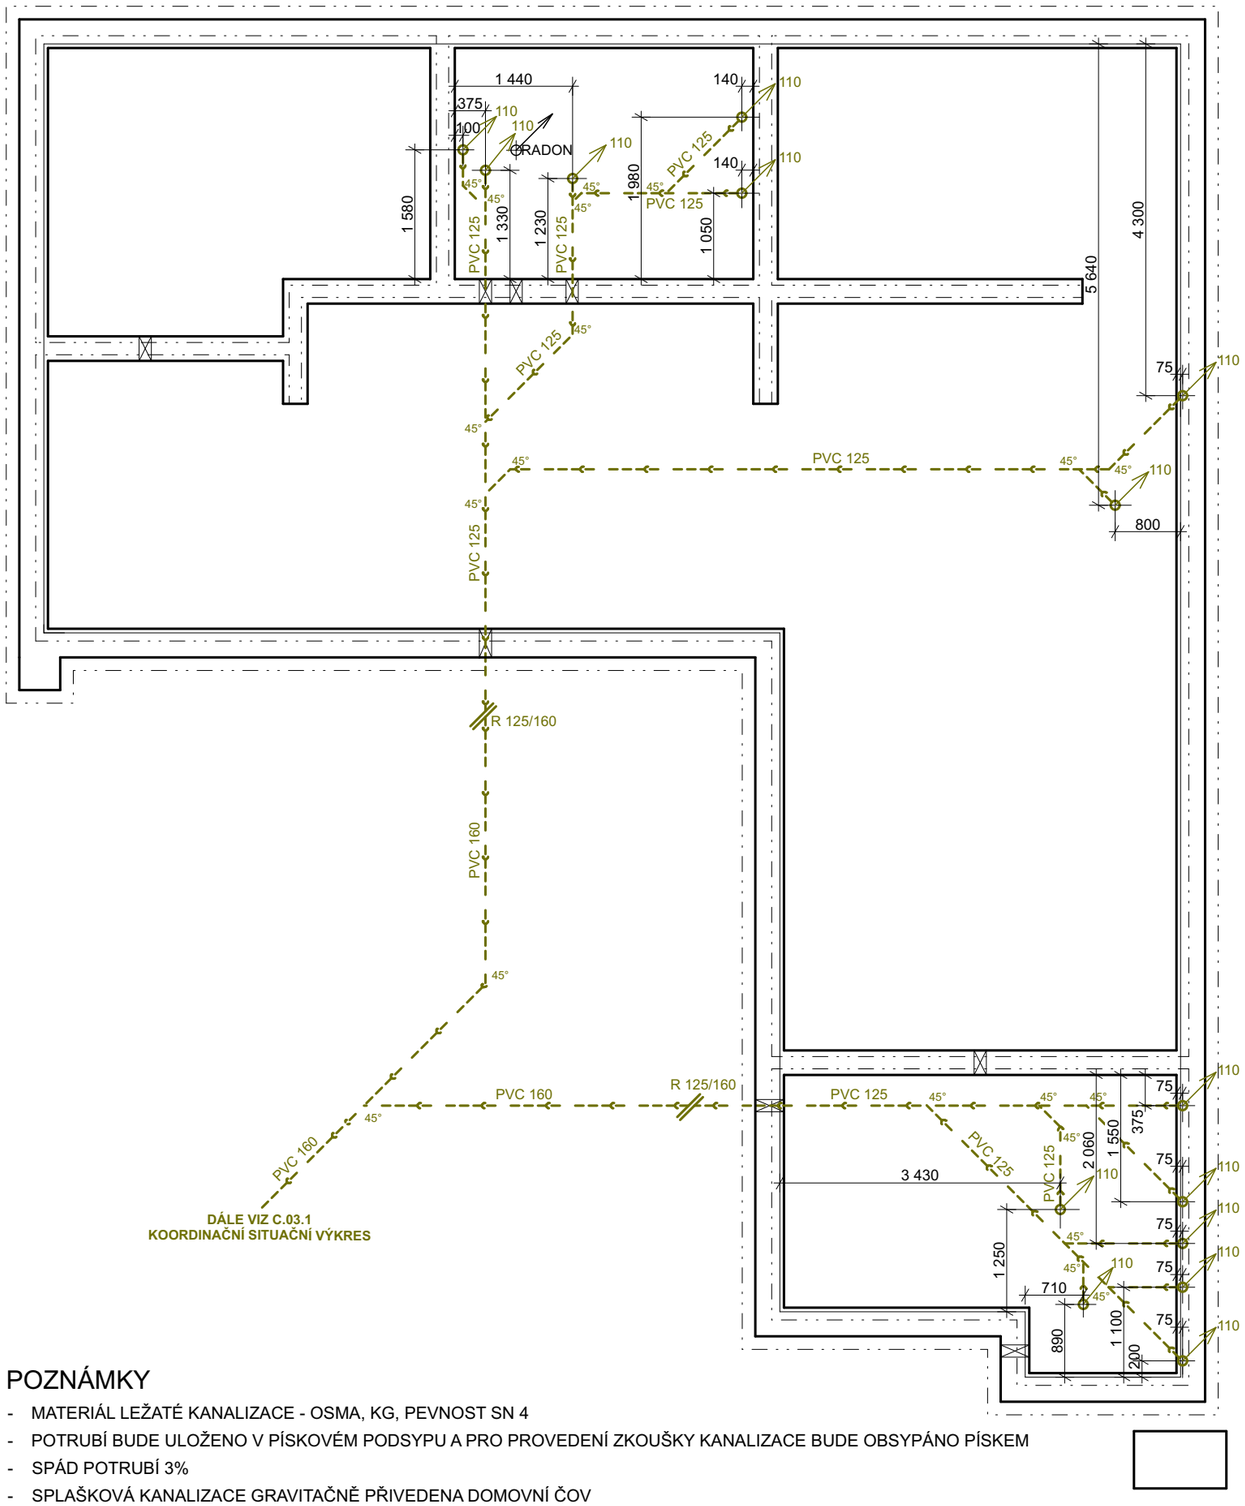

POZNÁMKY

- MATERIÁL LEŽATÉ KANALIZACE - OSMA, KG, PEVNOST SN 4
- POTRUBÍ BUDE ULOŽENO V PÍSKOVÉM PODSYPU A PRO PROVEDENÍ ZKOUŠKY KANALIZACE BUDE OBSYPÁNO PÍSKEM
- SPÁD POTRUBÍ 3%
- SPLAŠKOVÁ KANALIZACE GRAVITAČNĚ PŘIVEDENA DOMOVNÍ ČOV
- PROSTUP ZÁKLADOVÝM PASEM BUDE OPATŘEN CHRÁNIČKOU NEBO BUDE VYBEDNĚN
- VÝŠKA HRDEL STOUPACÍHO POTRUBÍ SPLAŠKOVÉ KANALIZACE BUDE PROVEDEN max. 10 mm NAD HORNÍ LÍC ZÁKLADOVÉ DESKY

Digitálně podepsal Ing. Miloš Slavík
Datum: 2026.03.09 08:58:04 +01'00'

Ing. MILOŠ SLAVÍK
Autorizovaný inženýr pro pozemní stavby
ČKAIT - 0012081

LUCERN
moderní dřevostavby

LUCERN DŘEVOSTAVBY s.r.o.
ÚDOLNÍ 280/15
PRAHA 4 - BRANÍK
147 00

± 0,000 = 397,402 m. n. m. (Bpv)

INVESTOR
Bc. Markéta Edwards,
K dálnici 167, Pitkovice,
104 00 Praha 10

STAVBA
NOVOSTAVBA RODINNÉHO DOMU
č. parc.: 154/10 a 154/16
k.ú.: Jevany [659312]

OBEC
Jevany [533378]

STUPEŇ PD
DSP + DPS

VEDOUCÍ PROJEKTU
Ing. Josef Frydrýn

VYPRACOVAL
Ing. Václav Křepelák, DiS.

AUTORIZACE
Ing. Miloš Slavík

DATUM
09/2025

MĚŘÍTKO
1:75

VÝKRES
SCHEMA LEŽATÉ KANALIZACE

D.1.4.1.2.