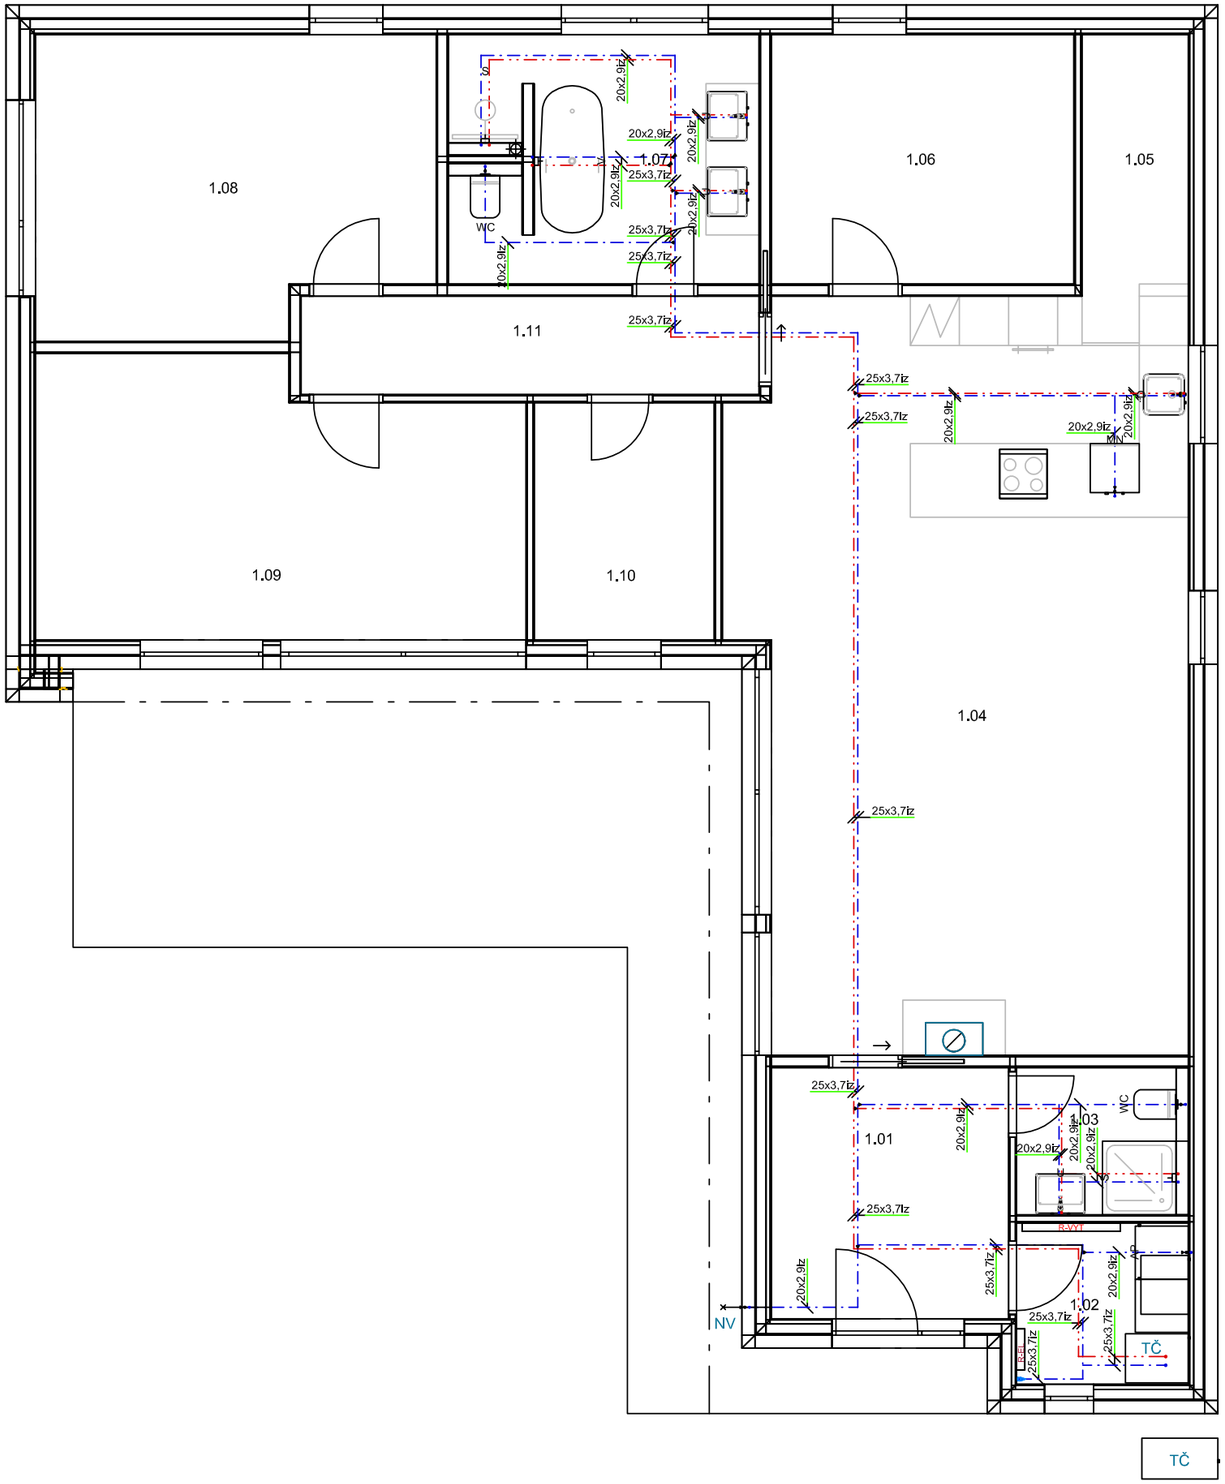

STUDENÁ VODA, POTRUBÍ RAUTITAN Stabil

TEPLÁ VODA, POTRUBÍ RAUTITAN Stabil

Digitálně podepsal Ing. Miloš Slavík
Datum: 2026.03.09 08:56:54 +01'00'

LUCERN
moderní dřevostavby

LUCERN DŘEVOSTAVBY s.r.o.
ÚDOLNÍ 280/15
PRAHA 4 - BRANÍK
147 00

± 0,000 = 397,402 m. n. m. (Bpv)

INVESTOR

Bc. Markéta Edwards,
K dálnici 167, Pitkovice,
104 00 Praha 10

STAVBA

NOVOSTAVBA RODINNÉHO DOMU
č. parc.: 154/10 a 154/16
k.ú.: Jevany [659312]

OBEC

Jevany [533378]

STUPEŇ PD

DSP + DPS

VEDOUCÍ PROJEKTU

Ing. Josef Frydrýn

VYPRACOVAL

Ing. Václav Křepelák, DiS.

AUTORIZACE

Ing. Miloš Slavík

DATUM

09/2025

MĚŘÍTKO

1:75

VÝKRES

SCHEMA VNITŘNÍHO VODOVODU

D.1.4.1.5.